COLUMNA TIPO 3
Es 1
ESC gen. 1:100
ESC secc. 1:25

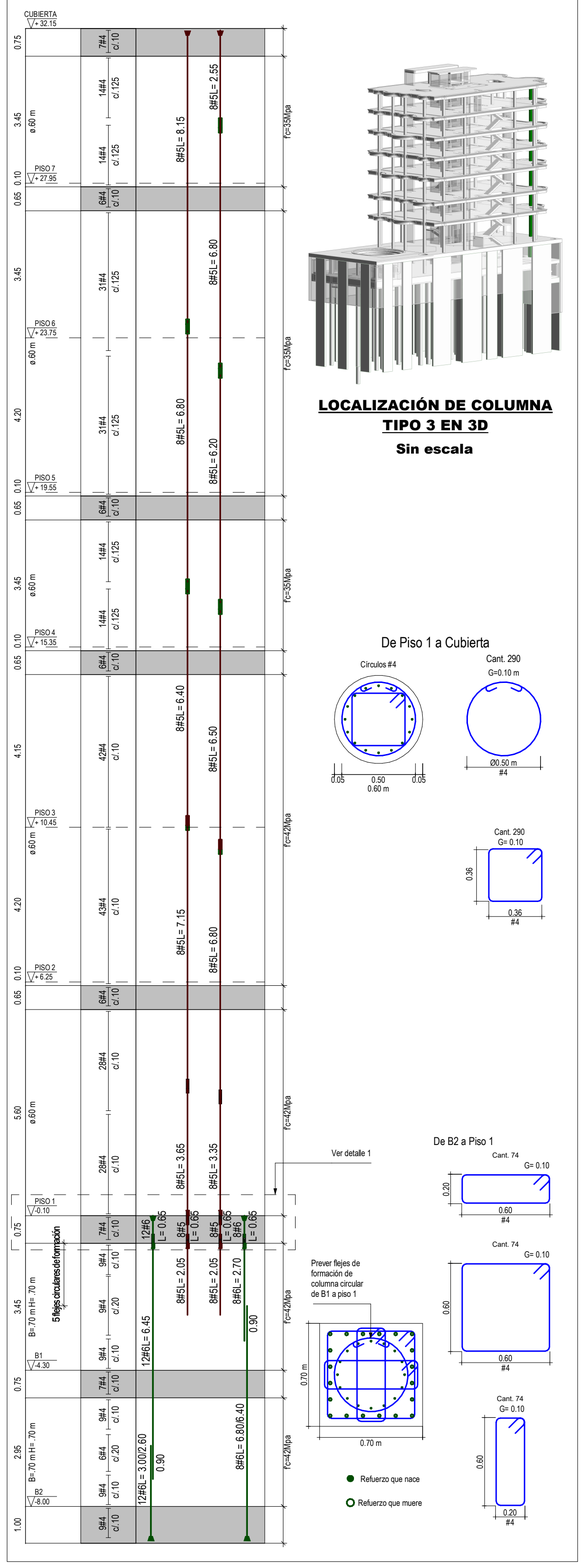

LOCALIZACIÓN DE COLUMNA TIPO 3 EN 3D

Sin escala

COLUMNA TIPO 4
Es 1
ESC gen. 1:100
ESC secc. 1:25

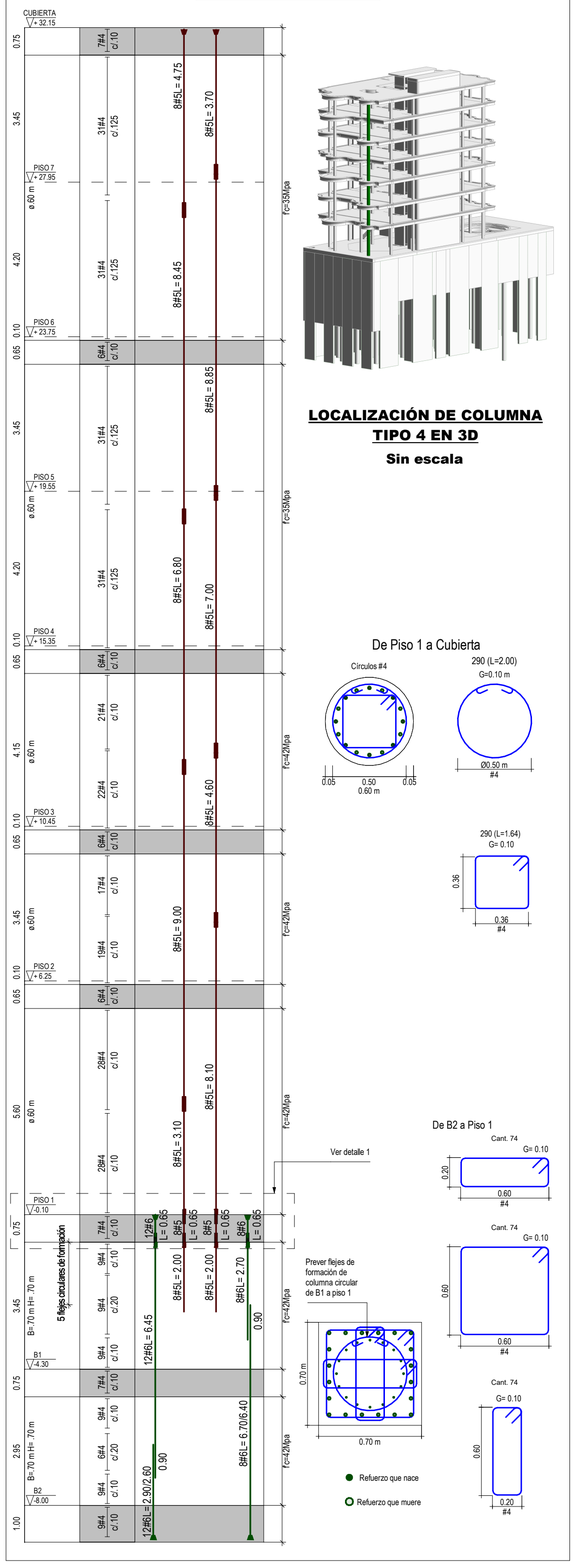

LOCALIZACIÓN DE COLUMNA TIPO 4 EN 3D

Sin escala

COLUMNA TIPO 5
Son 2
ESC gen. 1:100
ESC secc. 1:25

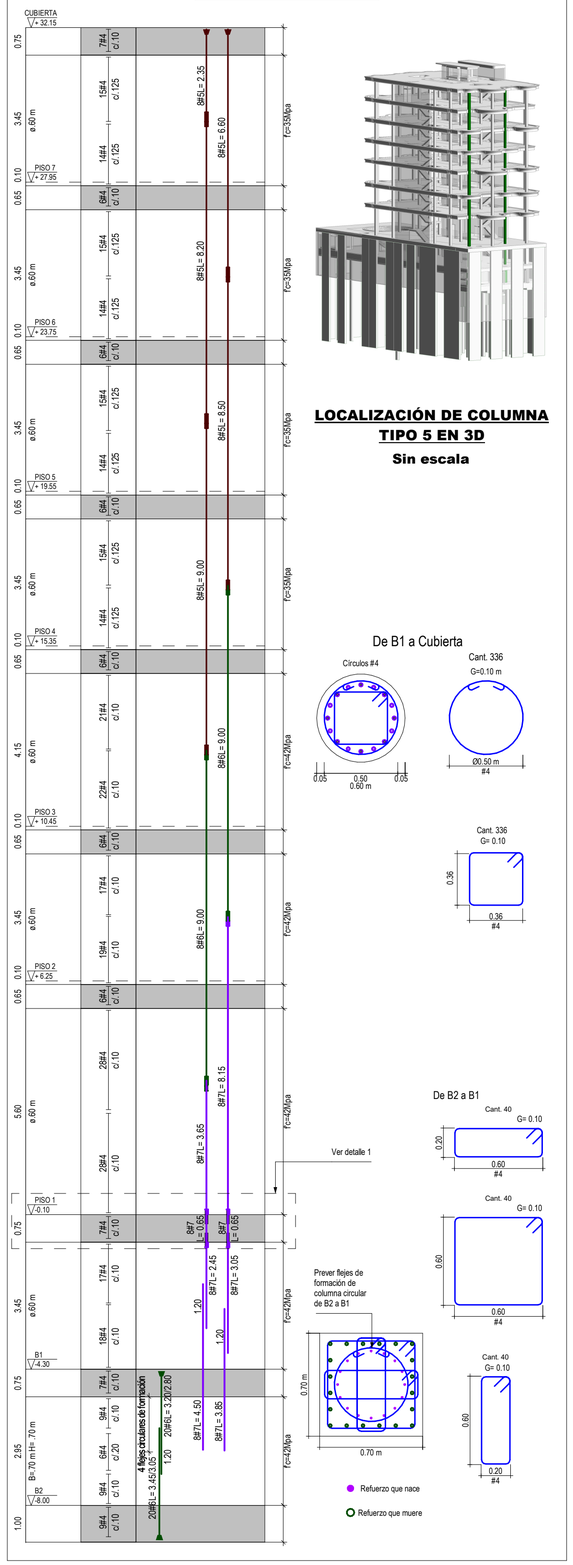

LOCALIZACIÓN DE COLUMNA TIPO 5 EN 3D

Sin escala

CONVENCIONES

Indica disco de anclaje

Indica empalme mecánico

NOTAS

1. Ver detalles generales en plano PL N° 01.02 y 01.03.
2. Ver planta localización e identificación de muros y columnas en PL. N° 04.00
3. Ver detalle 1 en PL.N°04.00

VERSIÓN : 1

PLANO N° 04.02

Aycardi Estructural

GERENTE DE PROYECTO
LUIS ENRIQUE AYCARDI F.
MAT. 2520212794 CND

INGENIERO
DANIEL E. QUICANO C.

MODELADOR
JUAN MANUEL SANTOS

MODIFICACIONES	FECHA
Emisión Inicial	13-03-2026

HUMANISE

Circular Lab

HUMANISE STUDIO

EAN-0519- AES-01-EST

Calle 71 #9-84

DESPIECE DE COLUMNAS

EAN-0519 -AES-01-EST-PL-509 04.02

REVISOR ESTRUCTURAL
JULIO CESAR SANMIGUEL CAMACHO
MAT. 25202-57738 CND

PLANO N° 04.02 VERSIÓN : 1