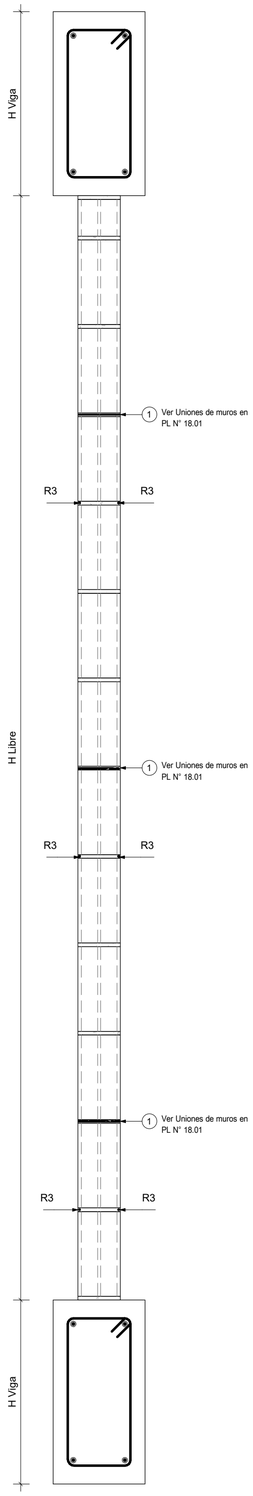

CORTE 1 - 1 - ALZADO REFUERZO EN MUROS DE MAMPOSTERÍA BLOQUE #5
Escala 1 : 10

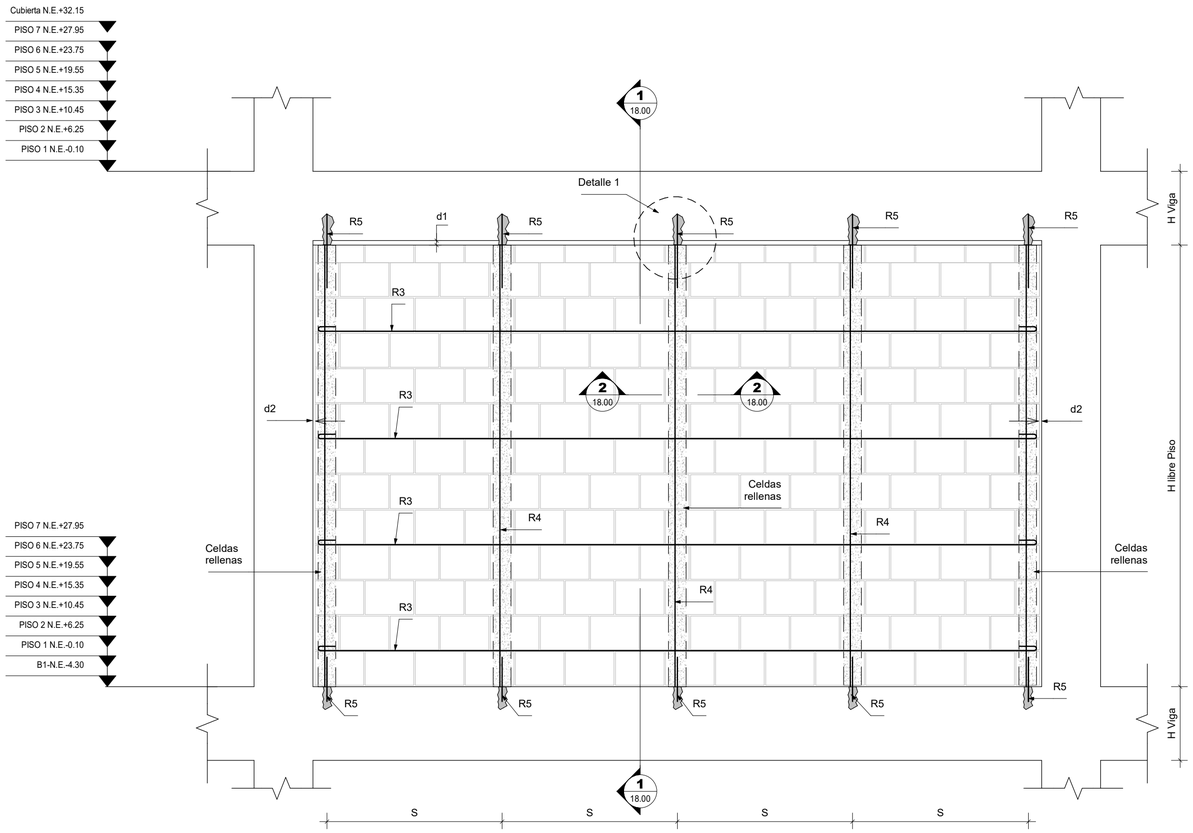

Tabla de separaciones (S) :

Cubierta: Smax=2.00m
Piso 7: Smax=2.00m
Piso 6: Smax= 2.00m
Piso 5: Smax=2.00m
Piso 4: Smax=1.80m
Piso 3: Smax=1.80m
Piso 2: Smax=1.80m
Piso 1: Smax=1.00m
Cimentación: Smax =2.00m

R3	Son 2 Ø4mm c/ 3 Hiladas
R4	1#5 L=Altura libre - 0.05m
R5	1#5 L=0.80m anclada 0.10m con resina epóxica
d1	Dilatación 0.01m (dejar icopor o similar de 0.01m)
d2	Dilatación 0.015m (dejar icopor o similar de 0.015m)

ELEVACIÓN DE MUROS INTERIORES EN BLOQUE #5
Escala 1 : 25

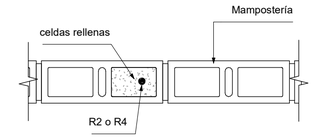

CORTE 2 - 2
Escala 1 : 10

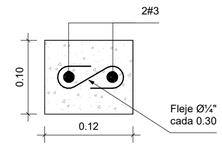

DETALLE VIGA CINTA
Escala 1 : 5

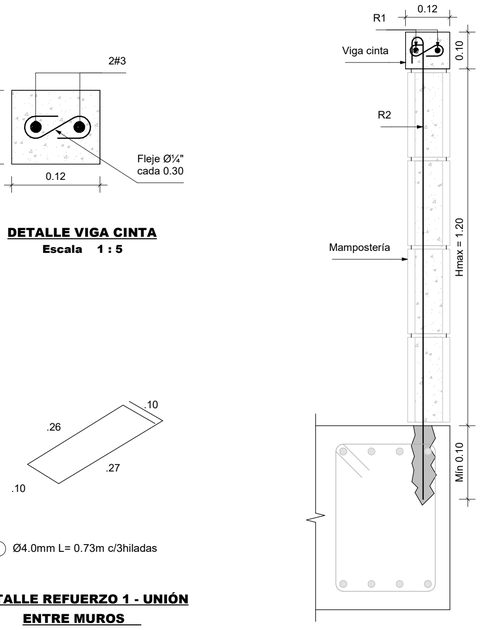

CORTE 3 - 3 SIN ENCHAPE
Escala 1 : 10

1 Ø4.0mm L= 0.73m c/3hiladas

DETALLE REFUERZO 1 - UNIÓN ENTRE MUROS
Escala 1 : 10

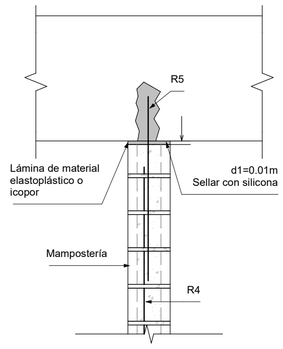

DETALLE 1
Escala 1 : 10

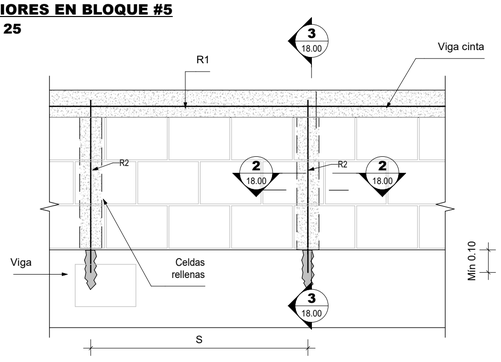

S	1.20m Separación máxima entre refuerzo
R1	Refuerzo viga cinta 2#3, flejes Ø¼" c/0.30
R2	Refuerzo antepecho 1#5 L= Variable anclada 0.10m con resina epóxica

ANTEPECHOS Y PARAPETOS
Escala 1 : 20

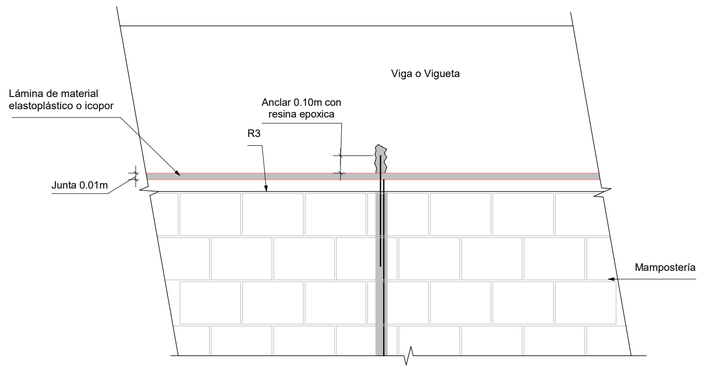

R3:2 Ø 4mm c/ 3 hiladas

DETALLE SUPERIOR DE BLOQUE #5 CON BLOQUE DE ICOPOR
Escala 1 : 20

Grupo de Uso
III

Grado de desempeño:
SUPERIOR

NOTAS:

- Previo a la construcción de los muros no estructurales deberá revisarse el trazado de las redes dispuestas en los muros.
- Las resistencias deben comprobarse mediante ensayos ejecutados de acuerdo con las normas colombianas de diseño y construcción sismo-resistente NSR-10
- Ver isométricos de uniones de muros en plano PL N° 18.01

NOTA:
Este plano debe ser revisado y aprobado por el Constructor del proyecto.

VºBº CONSTRUCTOR RESPONSABLE:

MUROS NO ESTRUCTURALES DE MAMPOSTERÍA

f'cr (Kg/cm²)	f'cp (Kg/cm²)	f'cm (Kg/cm²)	f'cu (Kg/cm²)
Resistencia última a la compresión del mortero de relleno	Resistencia última a la compresión del mortero de pega	Resistencia última a la compresión del murete en mampostería	Resistencia última a la compresión de la unidad de mampostería
100	100	60	130

VERSIÓN : 1

PLANO N° 18.00

Aycardi Estructural

GERENTE DE PROYECTO
LUIS ENRIQUE AYCARDI F.
MAT. 2520212794 CND

INGENIERO
DANIEL E. QUICANO C.

MODELADOR
JUAN MANUEL SANTOS

MODIFICACIONES	FECHA
Emisión Inicial	13-03-2026

HUMANISE

Circular Lab

HUMANISE STUDIO

EAN-0519- AES-01-EST

Calle 71 #9-84

DETALLES DE MUROS NO ESTRUCTURALES

EAN-0519 -AES-01-EST-PL-5106 18.00

REVISOR ESTRUCTURAL
JULIO CESAR SANMIGUEL CAMACHO
MAT. 25202-57738 CND

PLANO N° 18.00 VERSIÓN : 1