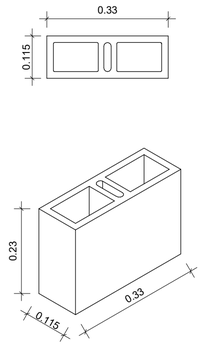

BLOQUE N° 5 PERFORACIÓN VERTICAL
Escala 1 : 10

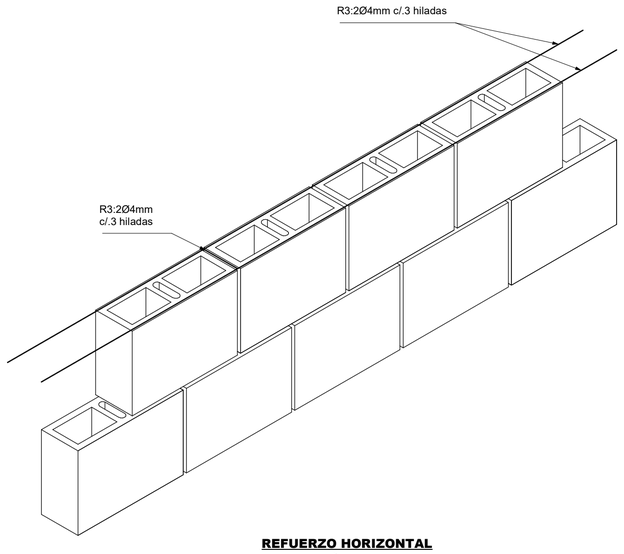

REFUERZO HORIZONTAL TÍPICO
Escala 1 : 10

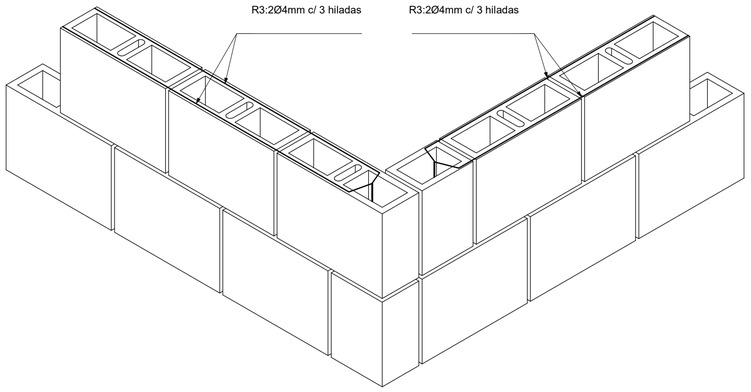

UNIÓN EN L - REFUERZO R3
Escala 1 : 10

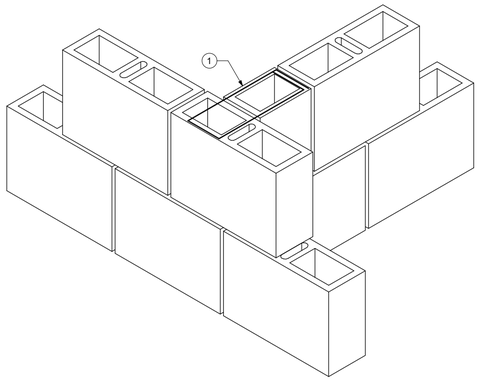

UNION EN T
Escala 1 : 10

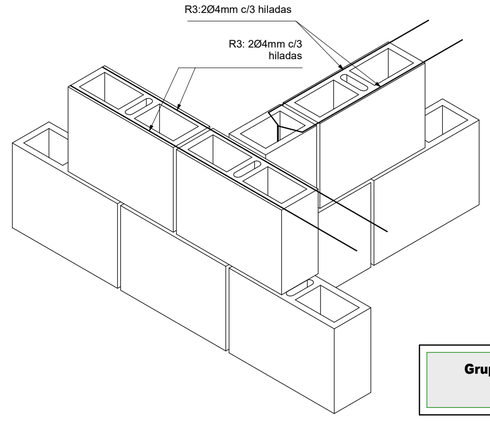

UNIÓN EN T - REFUERZO R3
Escala 1 : 10

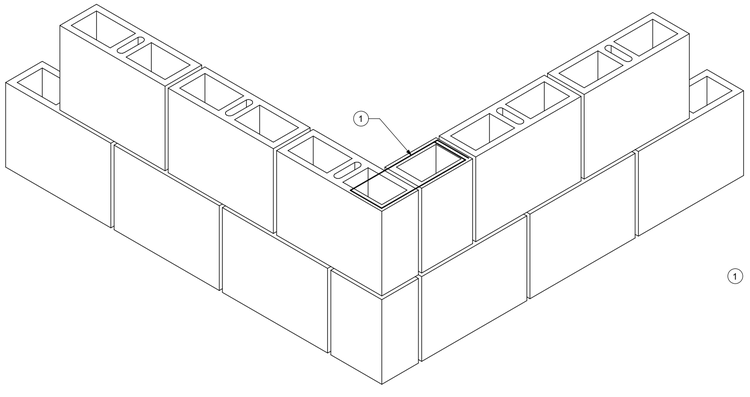

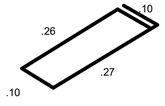

1 Ø4.0mm L= 0.73m c/3 hiladas

UNIÓN EN L
Escala 1 : 10

NOTAS
Ver detalles de muros en plano PL18.00

MUROS NO ESTRUCTURALES DE MAMPOSTERÍA			
f'cr (Kg/cm²)	**f'cp (Kg/cm²)**	**f'cm (Kg/cm²)**	**f'cu (Kg/cm²)**
Resistencia última a la compresión del mortero de relleno	Resistencia última a la compresión del mortero de pega	Resistencia última a la compresión del murete en mampostería	Resistencia última a la compresión de la unidad de mampostería
100	100	60	130

Grupo de Uso
III

Grado de desempeño:
SUPERIOR

ESPECIFICACIONES

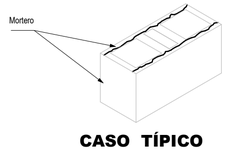

CASO TÍPICO

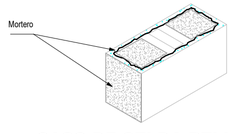

CASO DE CELDA RELLENAS

1. El mortero de pega se hara según la siguiente disposición:
2. Las juntas verticales y horizontales son de 10 mm. con tolerancia de 3 mm.
3. Toda celda reforzada debe llevar ventana de limpieza
4. El mortero de relleno lleva agregado maximo de 3/8"

REQUISITOS DIMENSIONALES PARA UNIDADES DE MAMPOSTERÍA

tp = pared exterior portante > 2.5 cm.
tv = pared entre celdas > 2.5 cm.
v = dimension del vacio > .50 cm.

VERSIÓN : 1

PLANO N° 18.01

Aycardi Estructural

GERENTE DE PROYECTO
LUIS ENRIQUE AYCARDI F.
MAT. 2520212794 CND

INGENIERO
DANIEL E. QUICANO C.

MODELADOR
JUAN MANUEL SANTOS

MODIFICACIONES	FECHA
Emisión Inicial	13-03-2026

HUMANISE

Circular Lab

HUMANISE STUDIO

EAN-0519- AES-01-EST

Calle 71 #9-84

DETALLES DE ELEMENTOS NO ESTRUCTURALES

EAN-0519 -AES-01-EST-PL-5107 18.01

REVISOR ESTRUCTURAL
JULIO CESAR SANMIGUEL CAMACHO
MAT. 25202-57738 CND

PLANO N° 18.01 VERSIÓN : 1