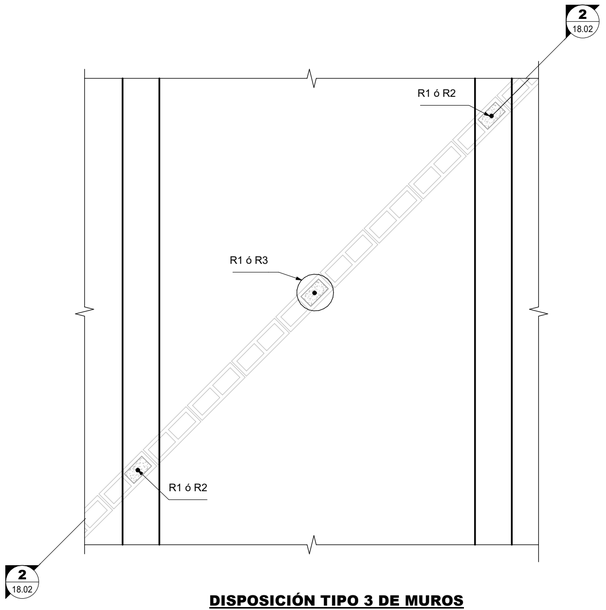

DISPOSICIÓN TIPO 3 DE MUROS
EN BLOQUE
Escala 1 : 20

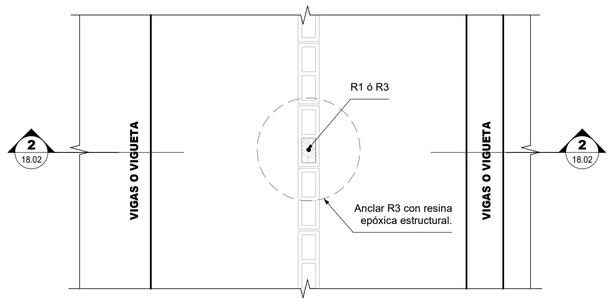

DISPOSICIÓN TIPO 2 DE MUROS
EN BLOQUE
Escala 1 : 20

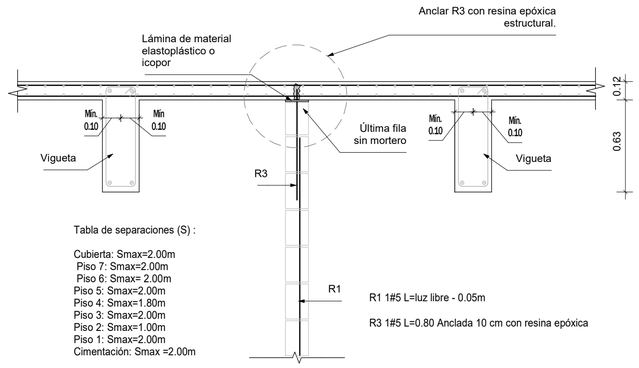

Tabla de separaciones (S) :

Cubierta: Smax=2.00m
Piso 7: Smax=2.00m
Piso 6: Smax= 2.00m
Piso 5: Smax=2.00m
Piso 4: Smax=1.80m
Piso 3: Smax=2.00m
Piso 2: Smax=1.00m
Piso 1: Smax=2.00m
Cimentación: Smax =2.00m

CORTE 2 - 2
Escala 1 : 20

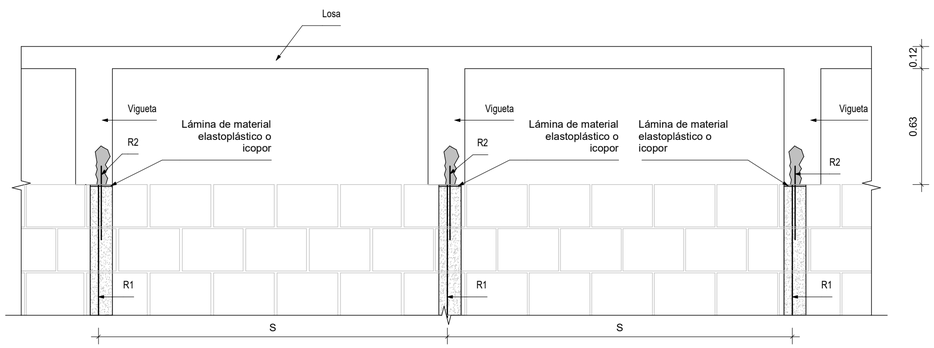

Tabla de separaciones (S) :

Cubierta: Smax=2.00m
Piso 7: Smax=2.00m
Piso 6: Smax= 2.00m
Piso 5: Smax=2.00m
Piso 4: Smax=1.80m
Piso 3: Smax=2.00m
Piso 2: Smax=1.00m
Piso 1: Smax=2.00m
Cimentación: Smax =2.00m

R1 1#5 L=luz libre -0.05m

R2 1#5 L=0.80 m anclada 0.10 m con resina epóxica

CORTE 1 - 1
Escala 1 : 20

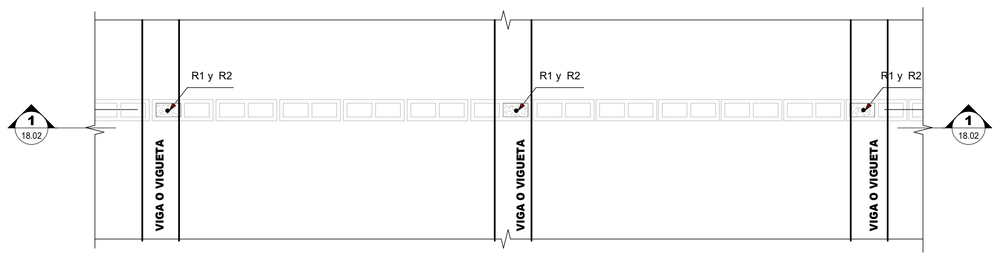

DISPOSICIÓN TIPO 1 DE MUROS
EN BLOQUE
Escala 1 : 20

Grupo de Uso	Grado de desempeño:
III	SUPERIOR

NOTAS:

1. Ver cuadro de especificaciones de mampostería en PL N° 18.00.
2. Previo a la construcción de los muros no estructurales deberá revisarse el trazado de las redes dispuestas en los muros.
3. Las resistencias deben comprobarse mediante ensayos ejecutados de acuerdo con las normas colombianas de diseño y construcción sismo-resistente NSR-10.

NOTA:
Este plano debe ser revisado y aprobado por el Constructor del proyecto.

VºBº CONSTRUCTOR RESPONSABLE:

VERSIÓN : 1

PLANO Nº 18.02

Aycardi Estructural

GERENTE DE PROYECTO
LUIS ENRIQUE AYCARDI F.
MAT. 2520212794 CND

INGENIERO
DANIEL E. QUICANO C.

MODELADOR
JUAN MANUEL SANTOS

MODIFICACIONES	FECHA
Emisión Inicial	13-03-2026

HUMANISE

Circular Lab

HUMANISE STUDIO

EAN-0519- AES-01-EST

Calle 71 #9-84

DETALLES DE MUROS NO ESTRUCTURALES

EAN-0519 -AES-01-EST-PL-5108 18.02

REVISOR ESTRUCTURAL
JULIO CESAR SANMIGUEL CAMACHO
MAT. 25202-57738 CND

PLANO Nº 18.02 VERSIÓN : 1