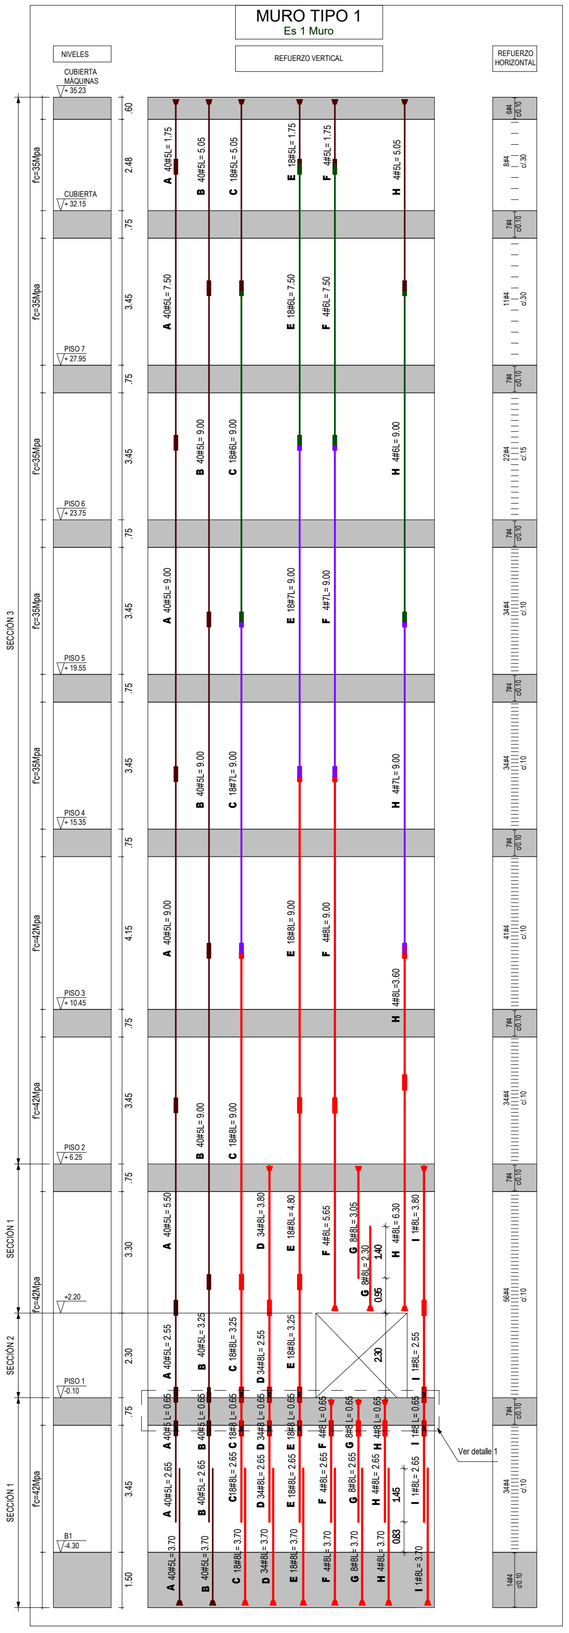

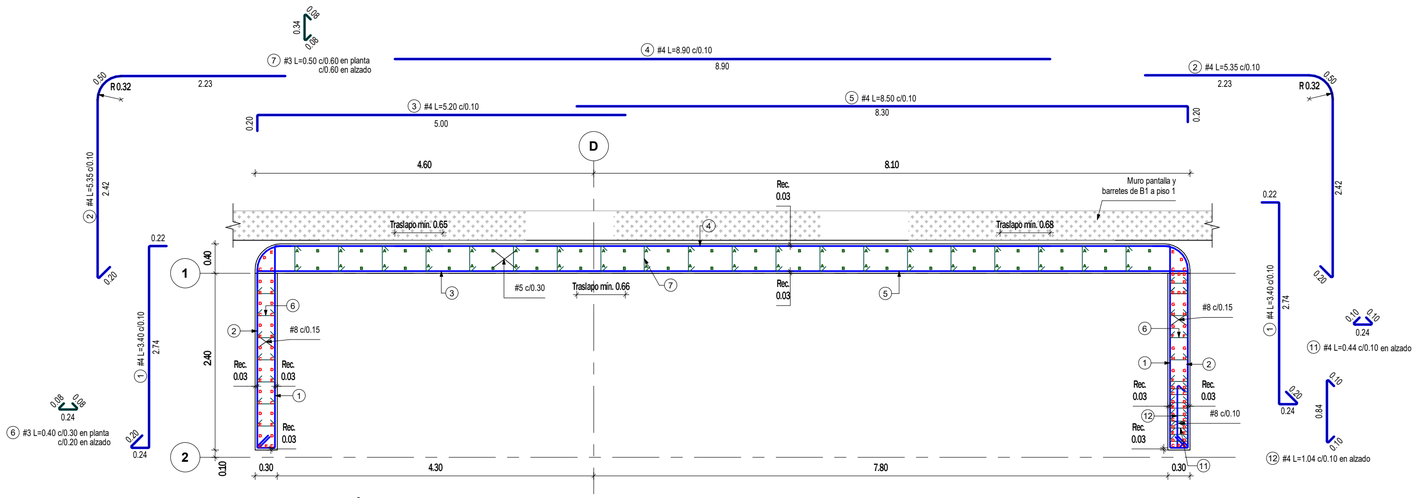

SECCIÓN 1 MURO M-1 DE B1 NE. -4.30 A PISO 1 NE. -0.10 Y DE NE.+2.20 A PISO 2 NE.+6.25

Escala 1 : 50

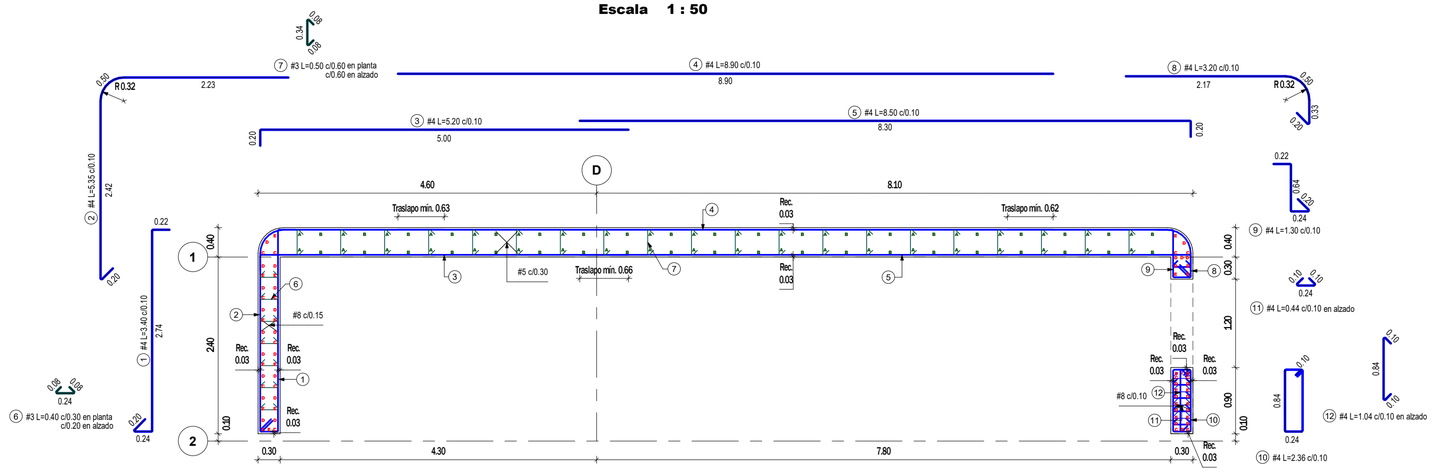

SECCIÓN 2 MURO M-1 DE PISO 1 NE. -0.10 A NE.+2.20

Escala 1 : 50

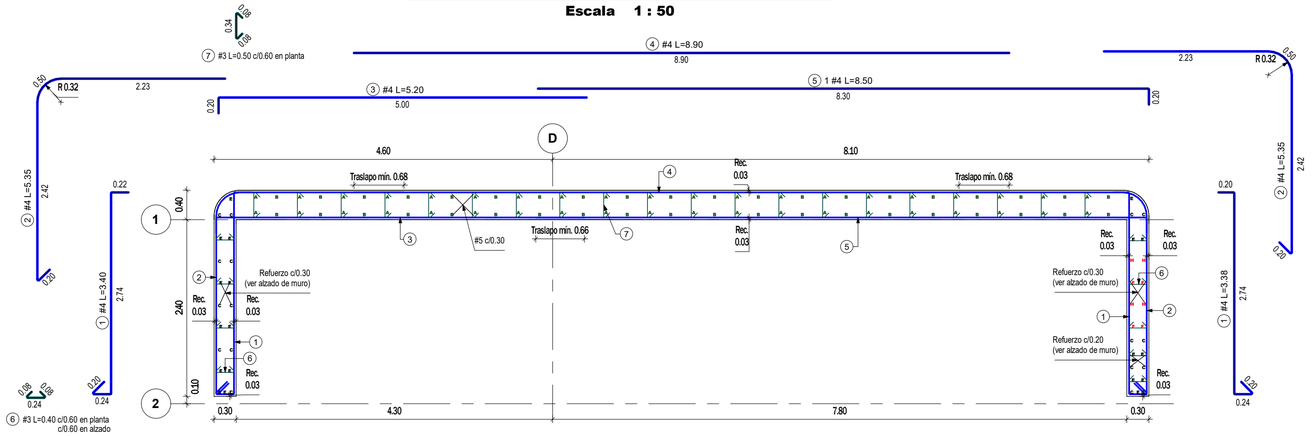

SECCIÓN 3 MURO M-1 DE PISO 2 NE. +6.25 A CUBIERTA DE MÁQUINAS NE. +35.23

Escala 1 : 50

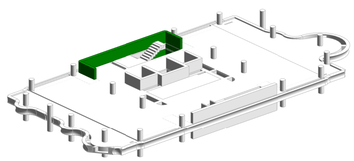

LOCALIZACIÓN DE MURO TIPO 1 EN 3D

Sin escala

Tabla de Separaciones Verticales Refuerzo Transversal **Sección 3**

Vano/Figuras	1-5	6	7
Piso 2-Piso 3	C/0.10	C/0.20	C/0.60
Piso 3-Piso 4	C/0.10	C/0.20	C/0.60
Piso 4-Piso 5	C/0.10	C/0.20	C/0.60
Piso 5-Piso 6	C/0.10	C/0.20	C/0.60
Piso 6-Piso 7	C/0.15	C/0.30	C/0.60
Piso 7-Cubierta	C/0.30	C/0.60	C/0.60
Cubierta-Cubierta Máquinas	C/0.30	C/0.60	C/0.60

CONVENCIONES

- Indica disco de anclaje
- Indica empalme mecánico

NOTAS

1. Ver detalles generales en plano PL N° 01.02 y 01.03
2. Ver planta localización e identificación de muros y columnas en PL. N° 04.00
3. Ver detalle 1 en el PL N° 04.00

VERSIÓN : 1

PLANO N° 04.05

Aycardi Estructural

GERENTE DE PROYECTO
LUIS ENRIQUE AYCARDI F.
MAT. 2520212794 CND

INGENIERO
DANIEL E. QUICANO C.

MODELADOR
JUAN MANUEL SANTOS

MODIFICACIONES	FECHA
Emisión Inicial	13-03-2026

HUMANISE

Circular Lab

HUMANISE STUDIO

EAN-0519- AES-01-EST

Calle 71 #9-84

DESPIECE MURO TIPO 1

EAN-0519 -AES-01-EST-PL-512 04.05

REVISOR ESTRUCTURAL
JULIO CESAR SANMIGUEL CAMACHO
MAT. 25202-57738 CND

PLANO N° 04.05 VERSIÓN : 1