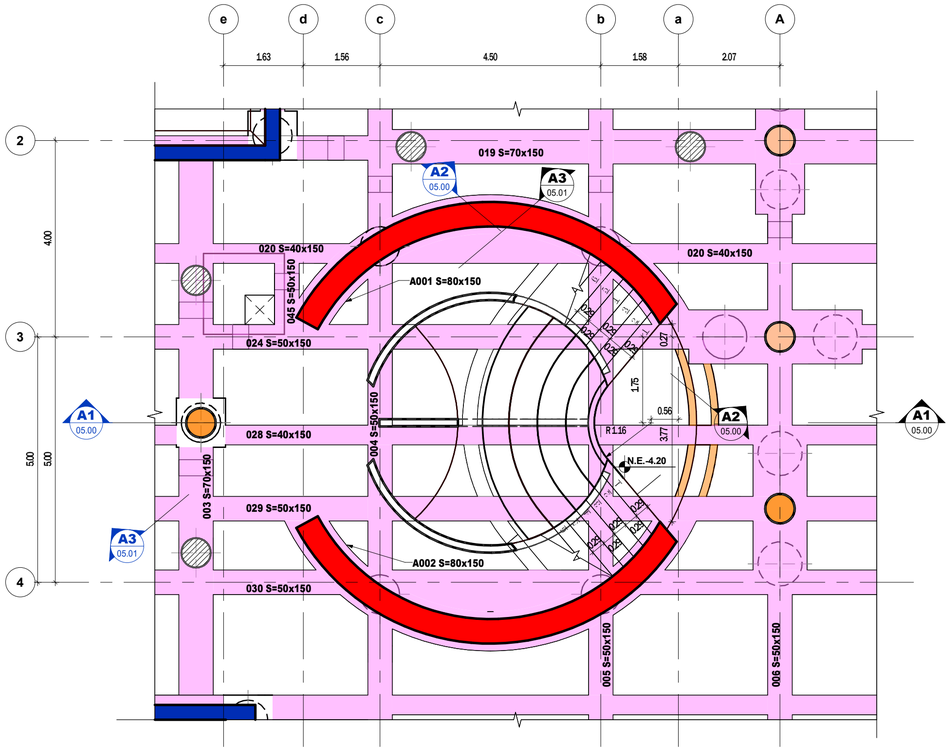

PLANTA ARRANQUE DE ESCALERAS Y GRADERIAS
Escala 1 : 75

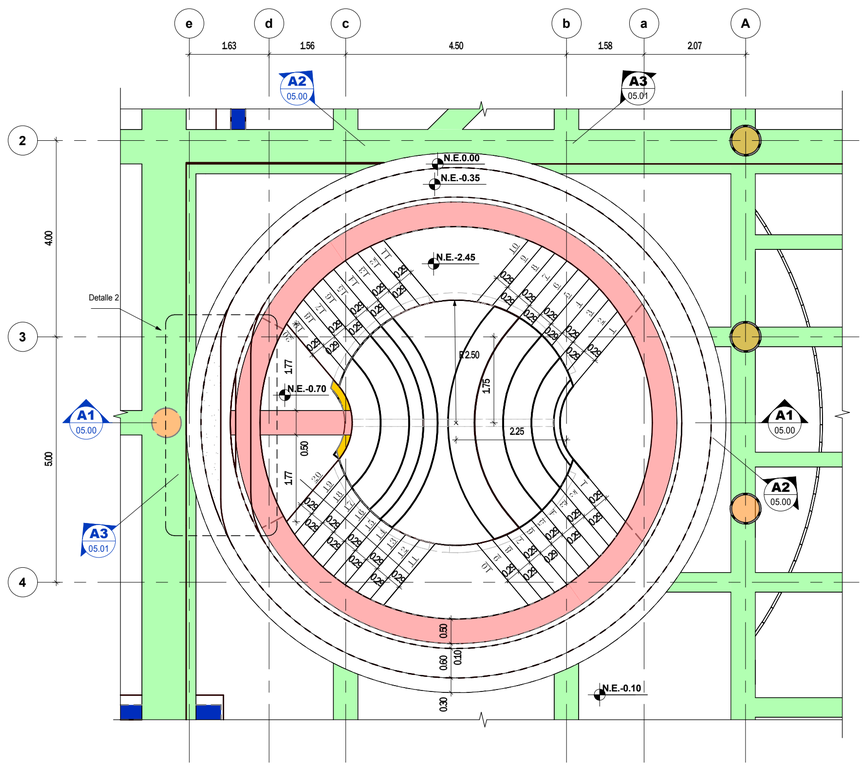

PLANTA LLEGADA ESCALERAS Y GRADERIA
Escala 1 : 75

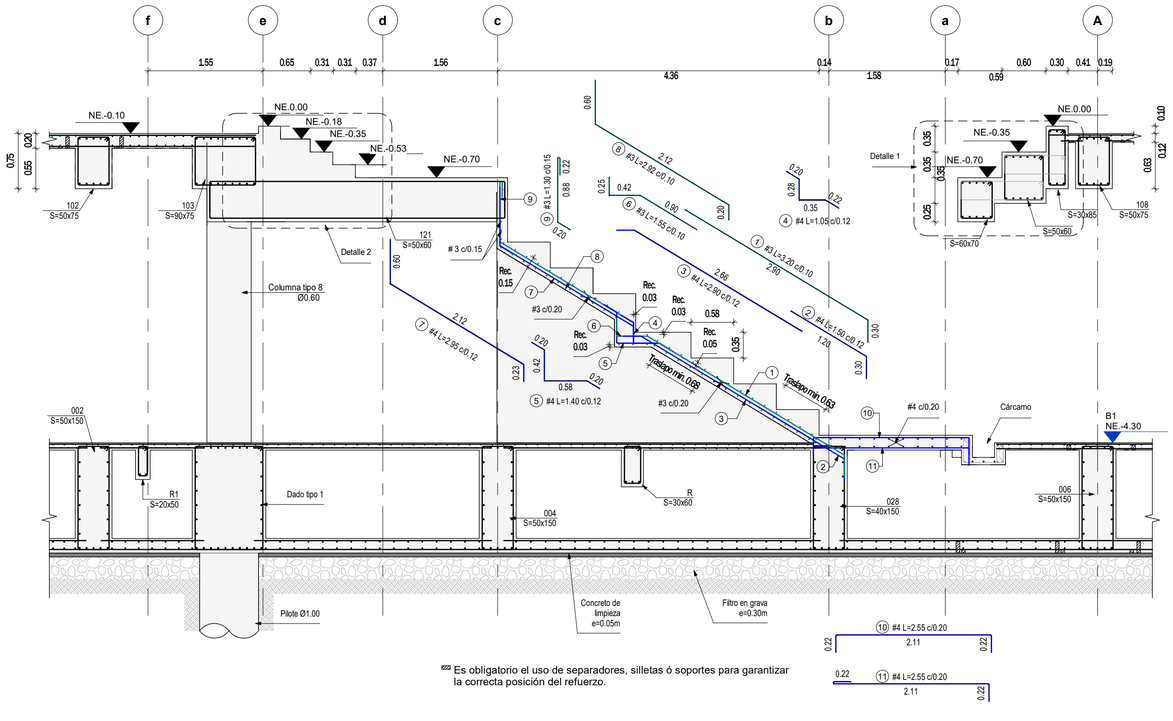

Es obligatorio el uso de separadores, silletas ó soportes para garantizar la correcta posición del refuerzo.

CORTE A1
Escala 1 : 50

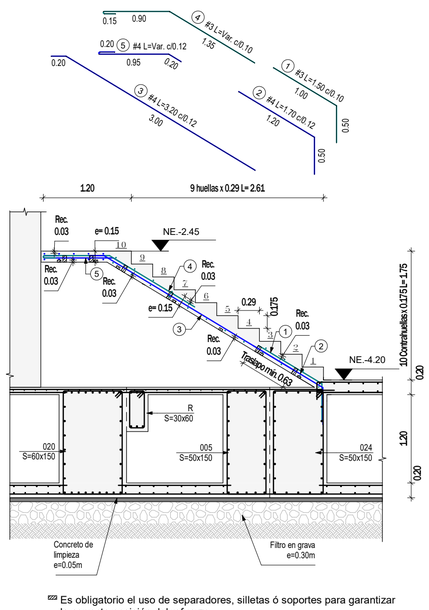

Es obligatorio el uso de separadores, silletas ó soportes para garantizar la correcta posición del refuerzo.

CORTE A2
Escala 1 : 50

CONCRETO

f'c=28 MPa
f'c=280 kg/cm²
f'c=4000 psi

NOTAS:

1. Ver plantas de piso 1 etapa 4 en PL N° 07.06 y PL N° 07.07.

VERSIÓN : 1

PLANO N° 05.00

Aycardi Estructural

GERENTE DE PROYECTO
LUIS ENRIQUE AYCARDI F.
MAT. 2520212794 CND

INGENIERO
DANIEL E. QUICANO C.

MODELADOR
PAULA ANDREA MONTOYA RENDÓN

MODIFICACIONES	FECHA
Emisión Inicial	13-03-2026

HUMANISE

Circular Lab

HUMANISE STUDIO

EAN-0519- AES-01-EST

Calle 71 #9-84

DETALLES ANFITEATRO

EAN-0519 -AES-01-EST-PL-515 05.00

REVISOR ESTRUCTURAL
JULIO CESAR SANMIGUEL CAMACHO
MAT. 25202-57738 CND

PLANO N° 05.00 VERSIÓN : 1